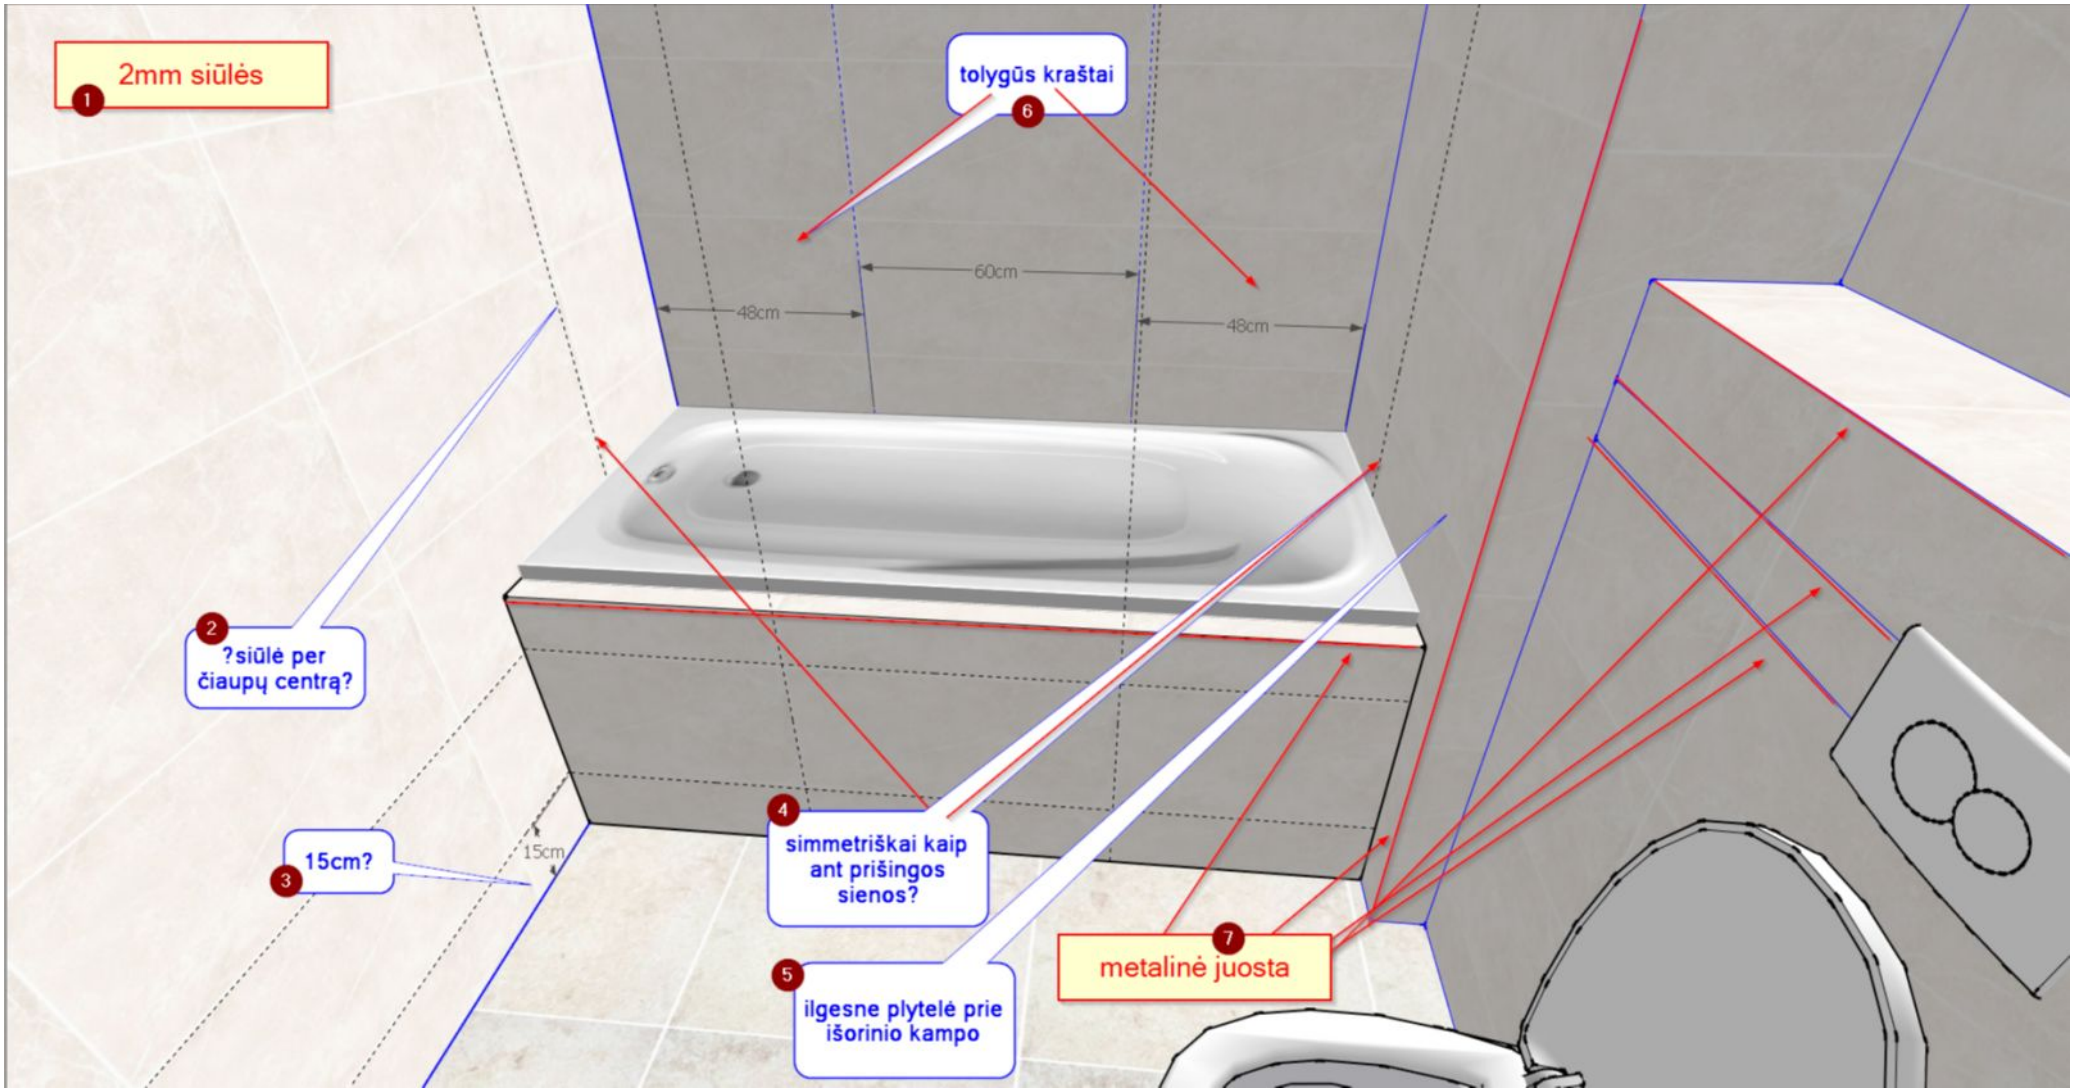
1
2mm siūlės
6
tolygūs kraštai
60cm
48cm
48cm
2
?siūlė per čiaupų centrą?
3
15cm?
15cm
4
simmetriškai kaip ant prišingos sienos?
5
ilgesne plytelė prie išorinio kampo
7
metalinė juosta

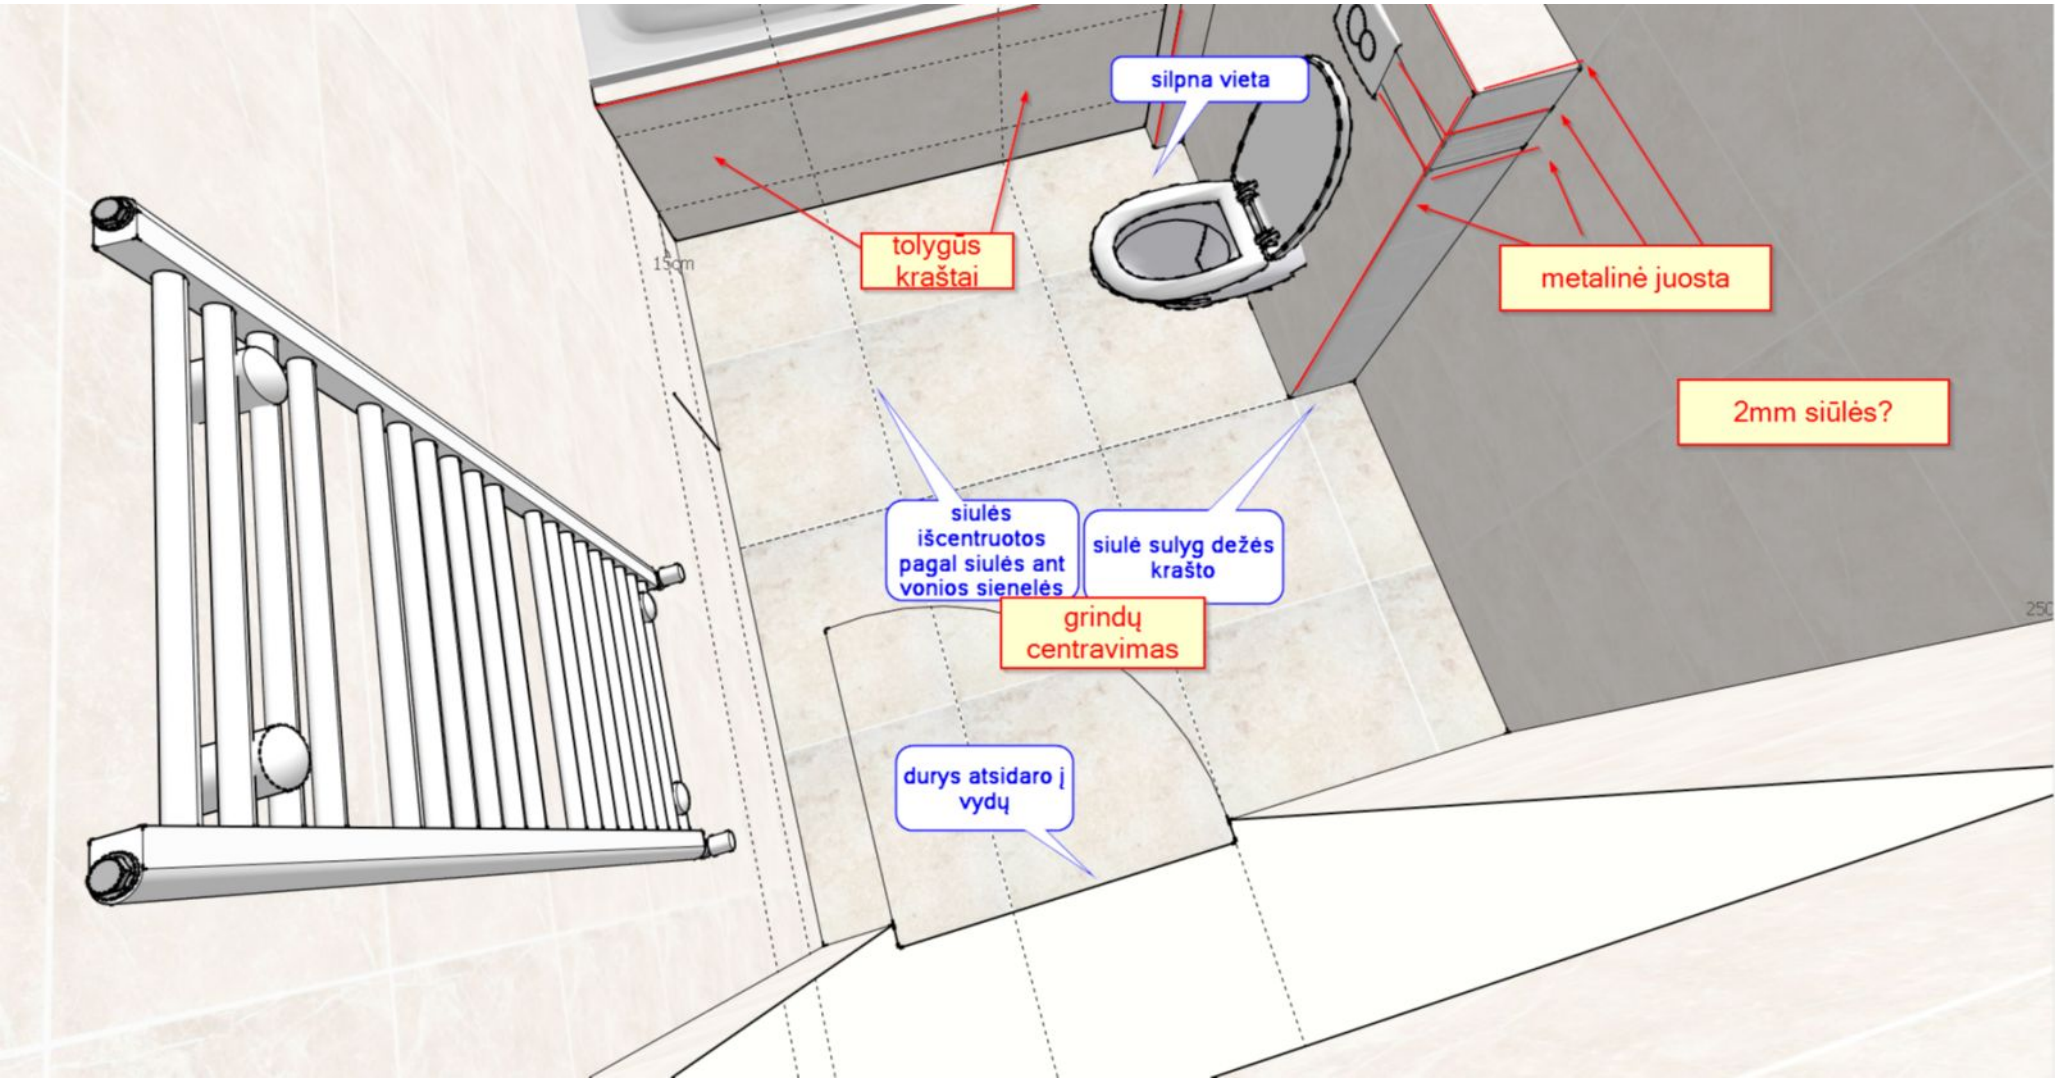
silpna vieta
tolygūs kraštai
metalinė juosta
2mm siūlės?
siulės išcentruotos pagal siulės ant vonios sienelės
siulė sulyg dežės krašto
grindų centravimas
durys atsidaro į vydų
15cm

metalinė juosta
metalinė juosta
60cm
48cm
15cm
15cm
15cm
viso ilgio (60cm) plytelė nuo krašto

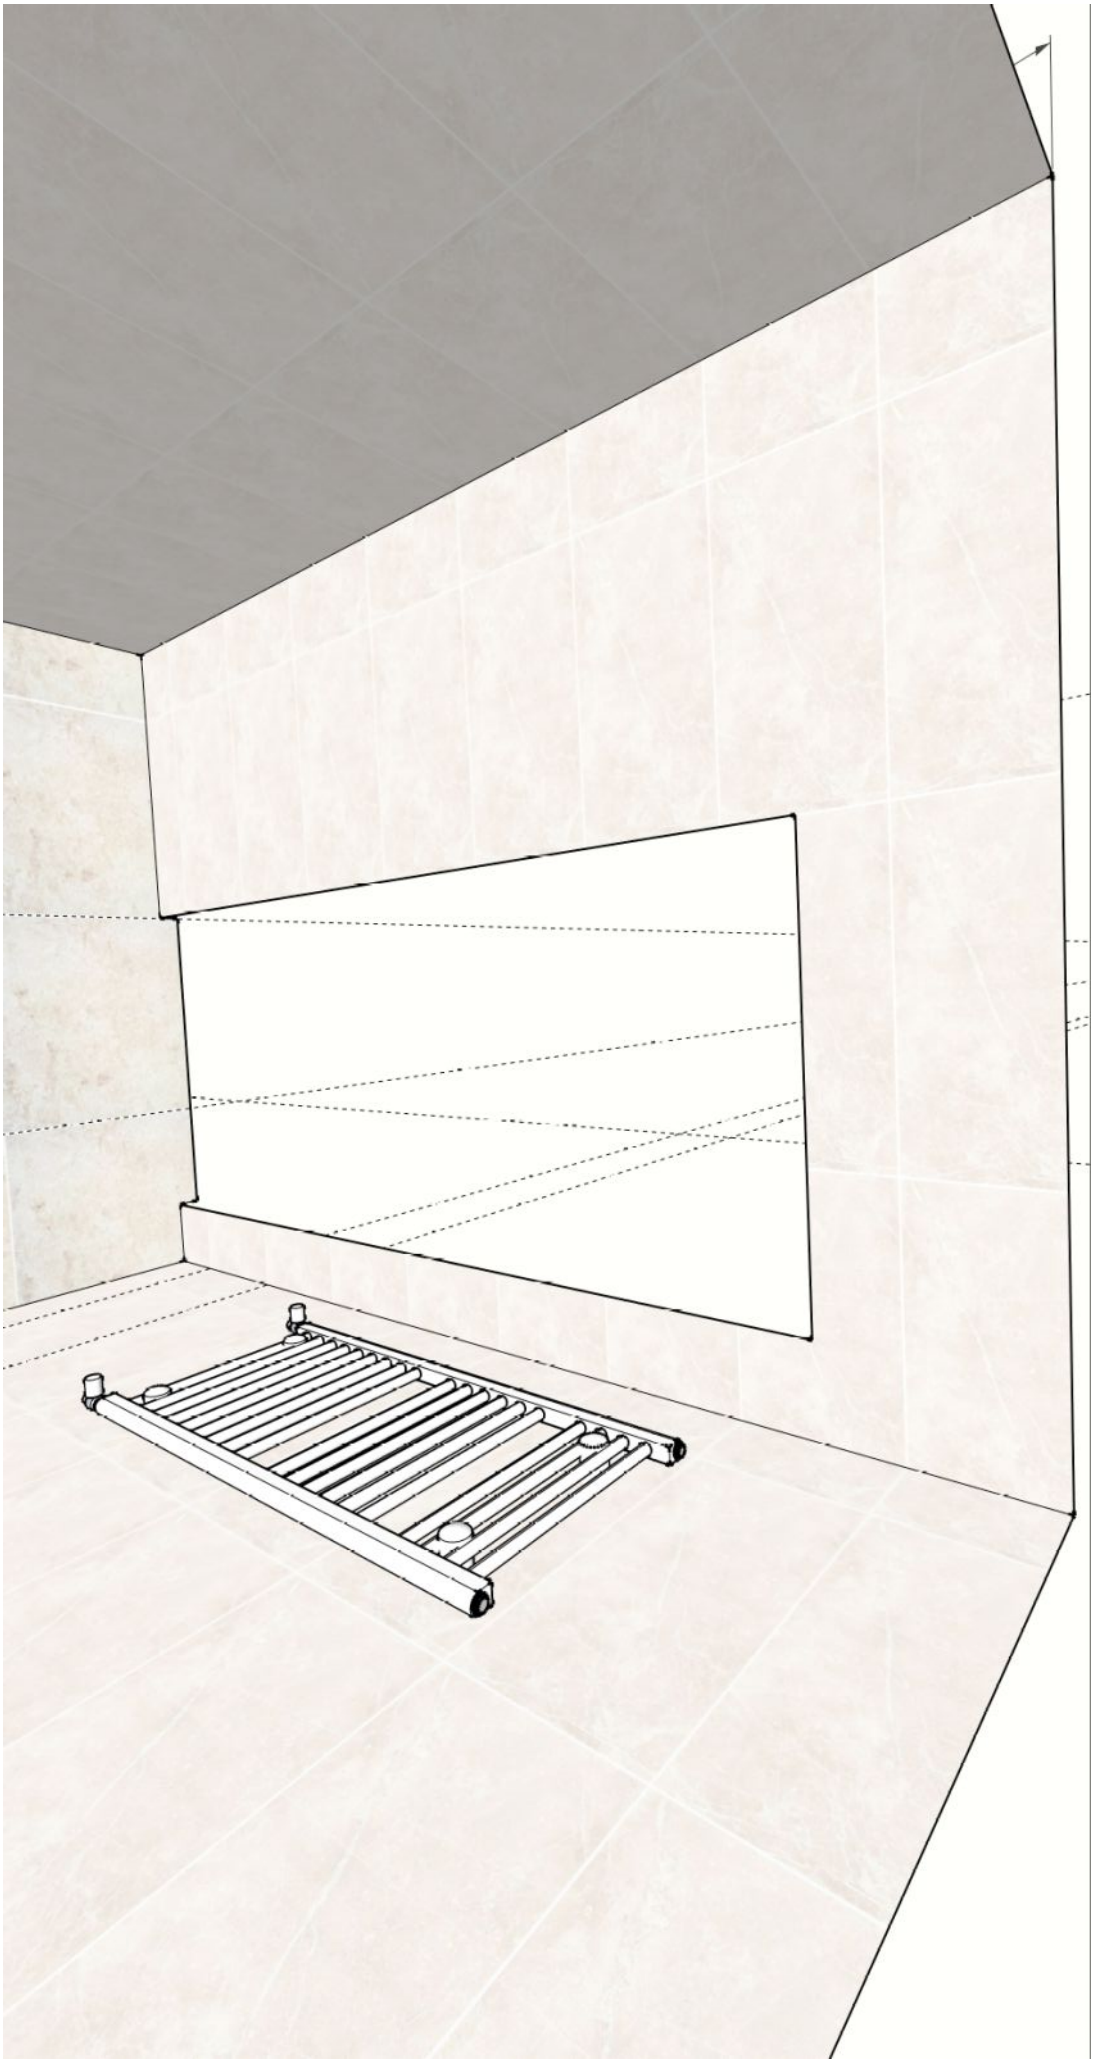

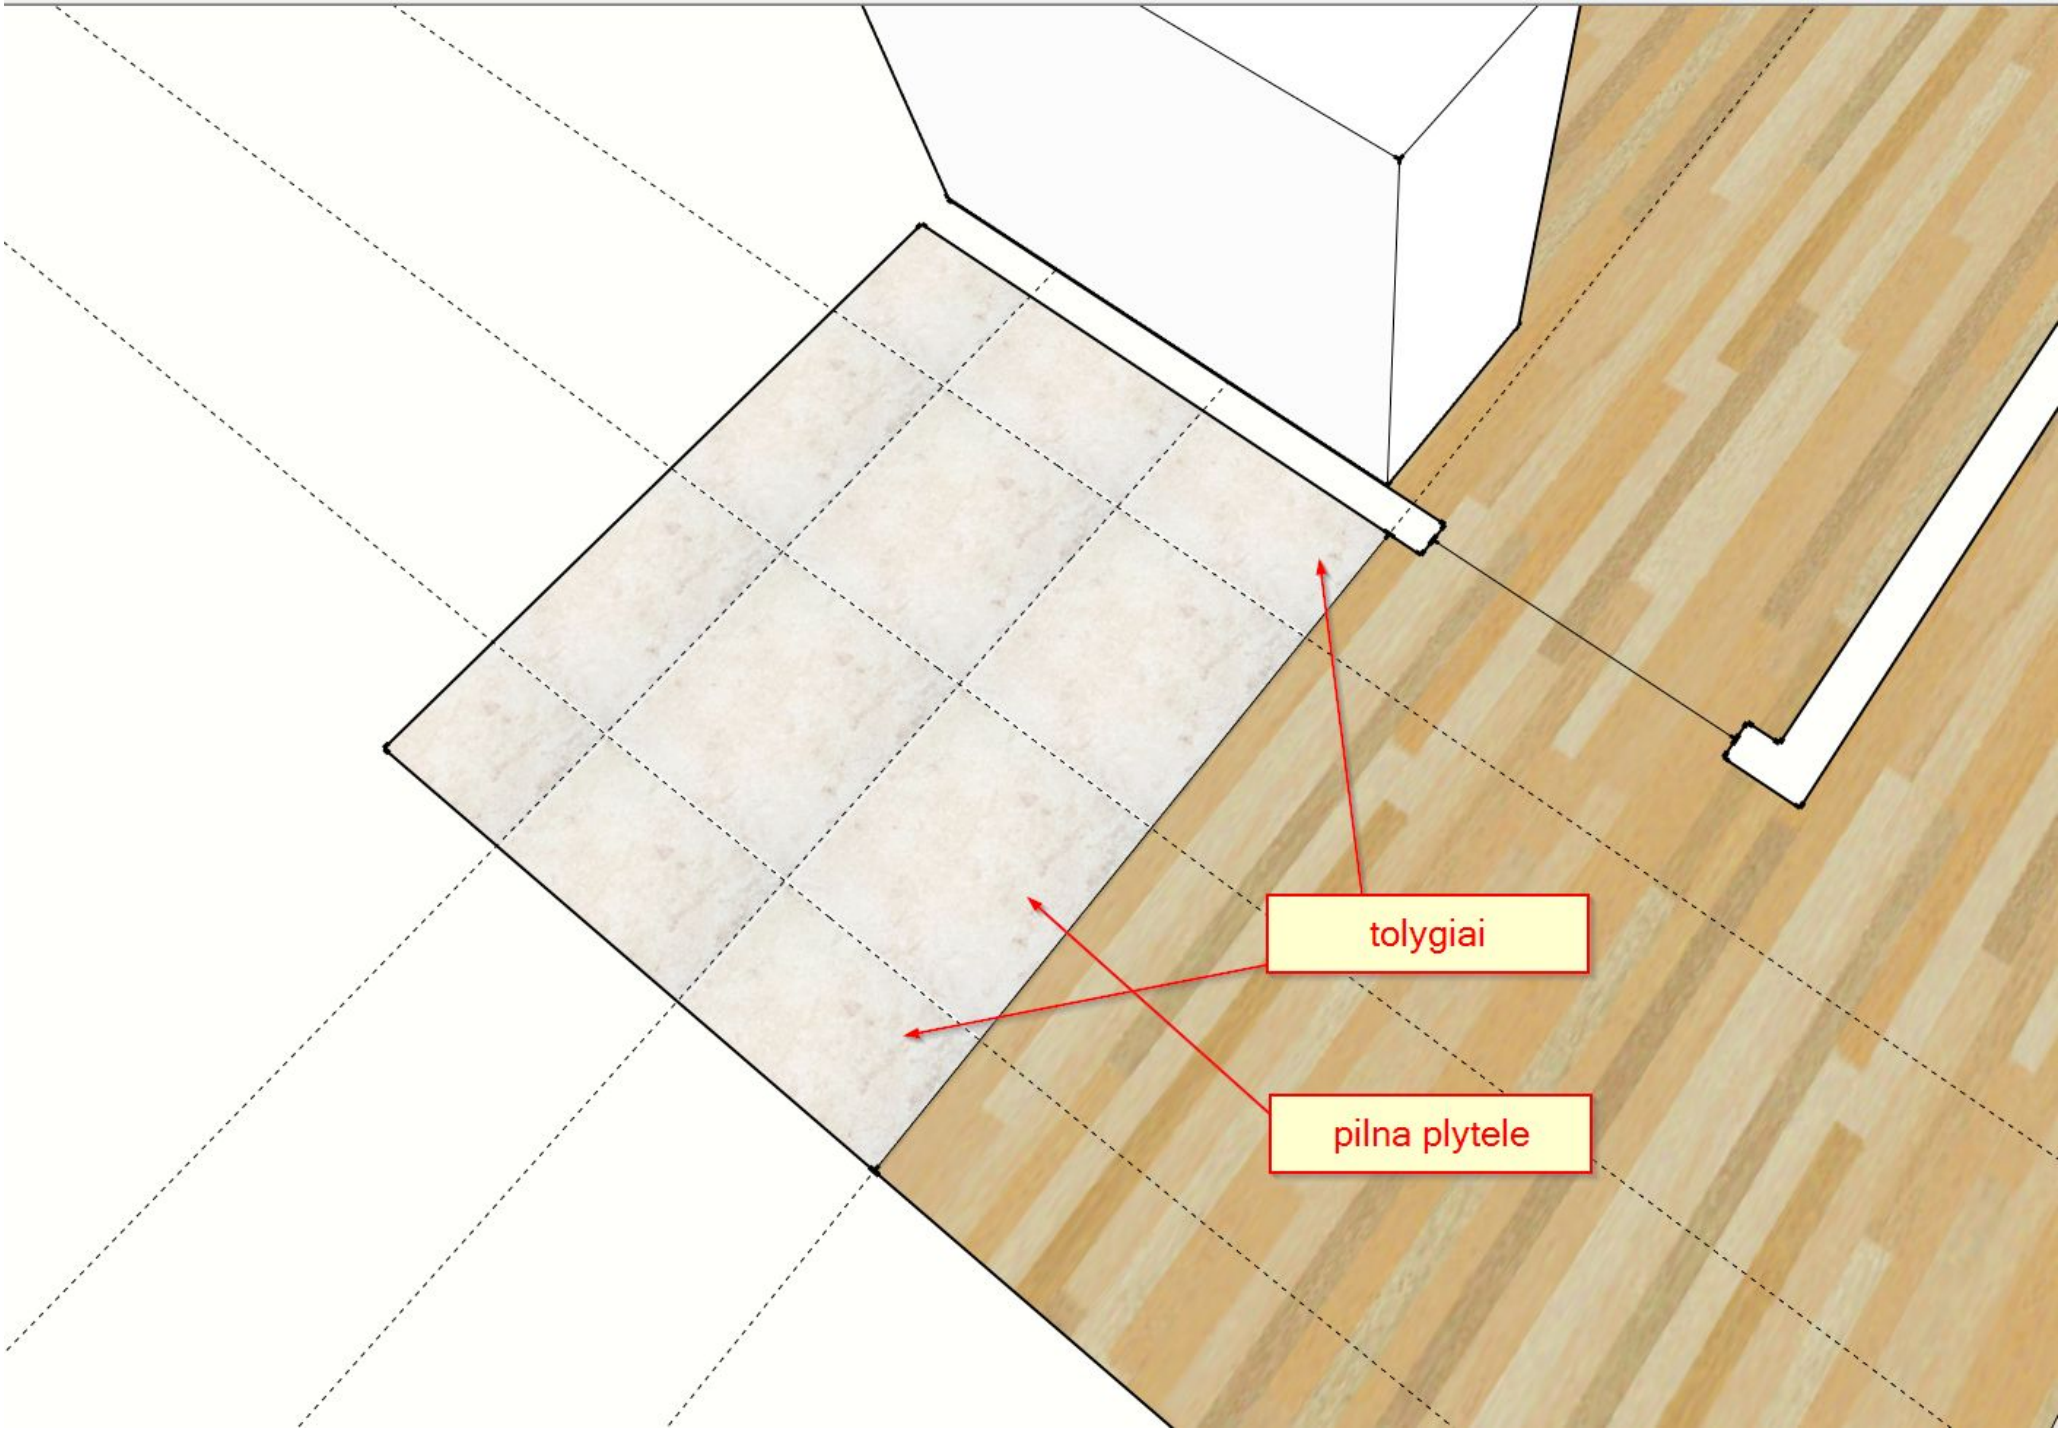
tolygiai
pilna plytele